Diag. A

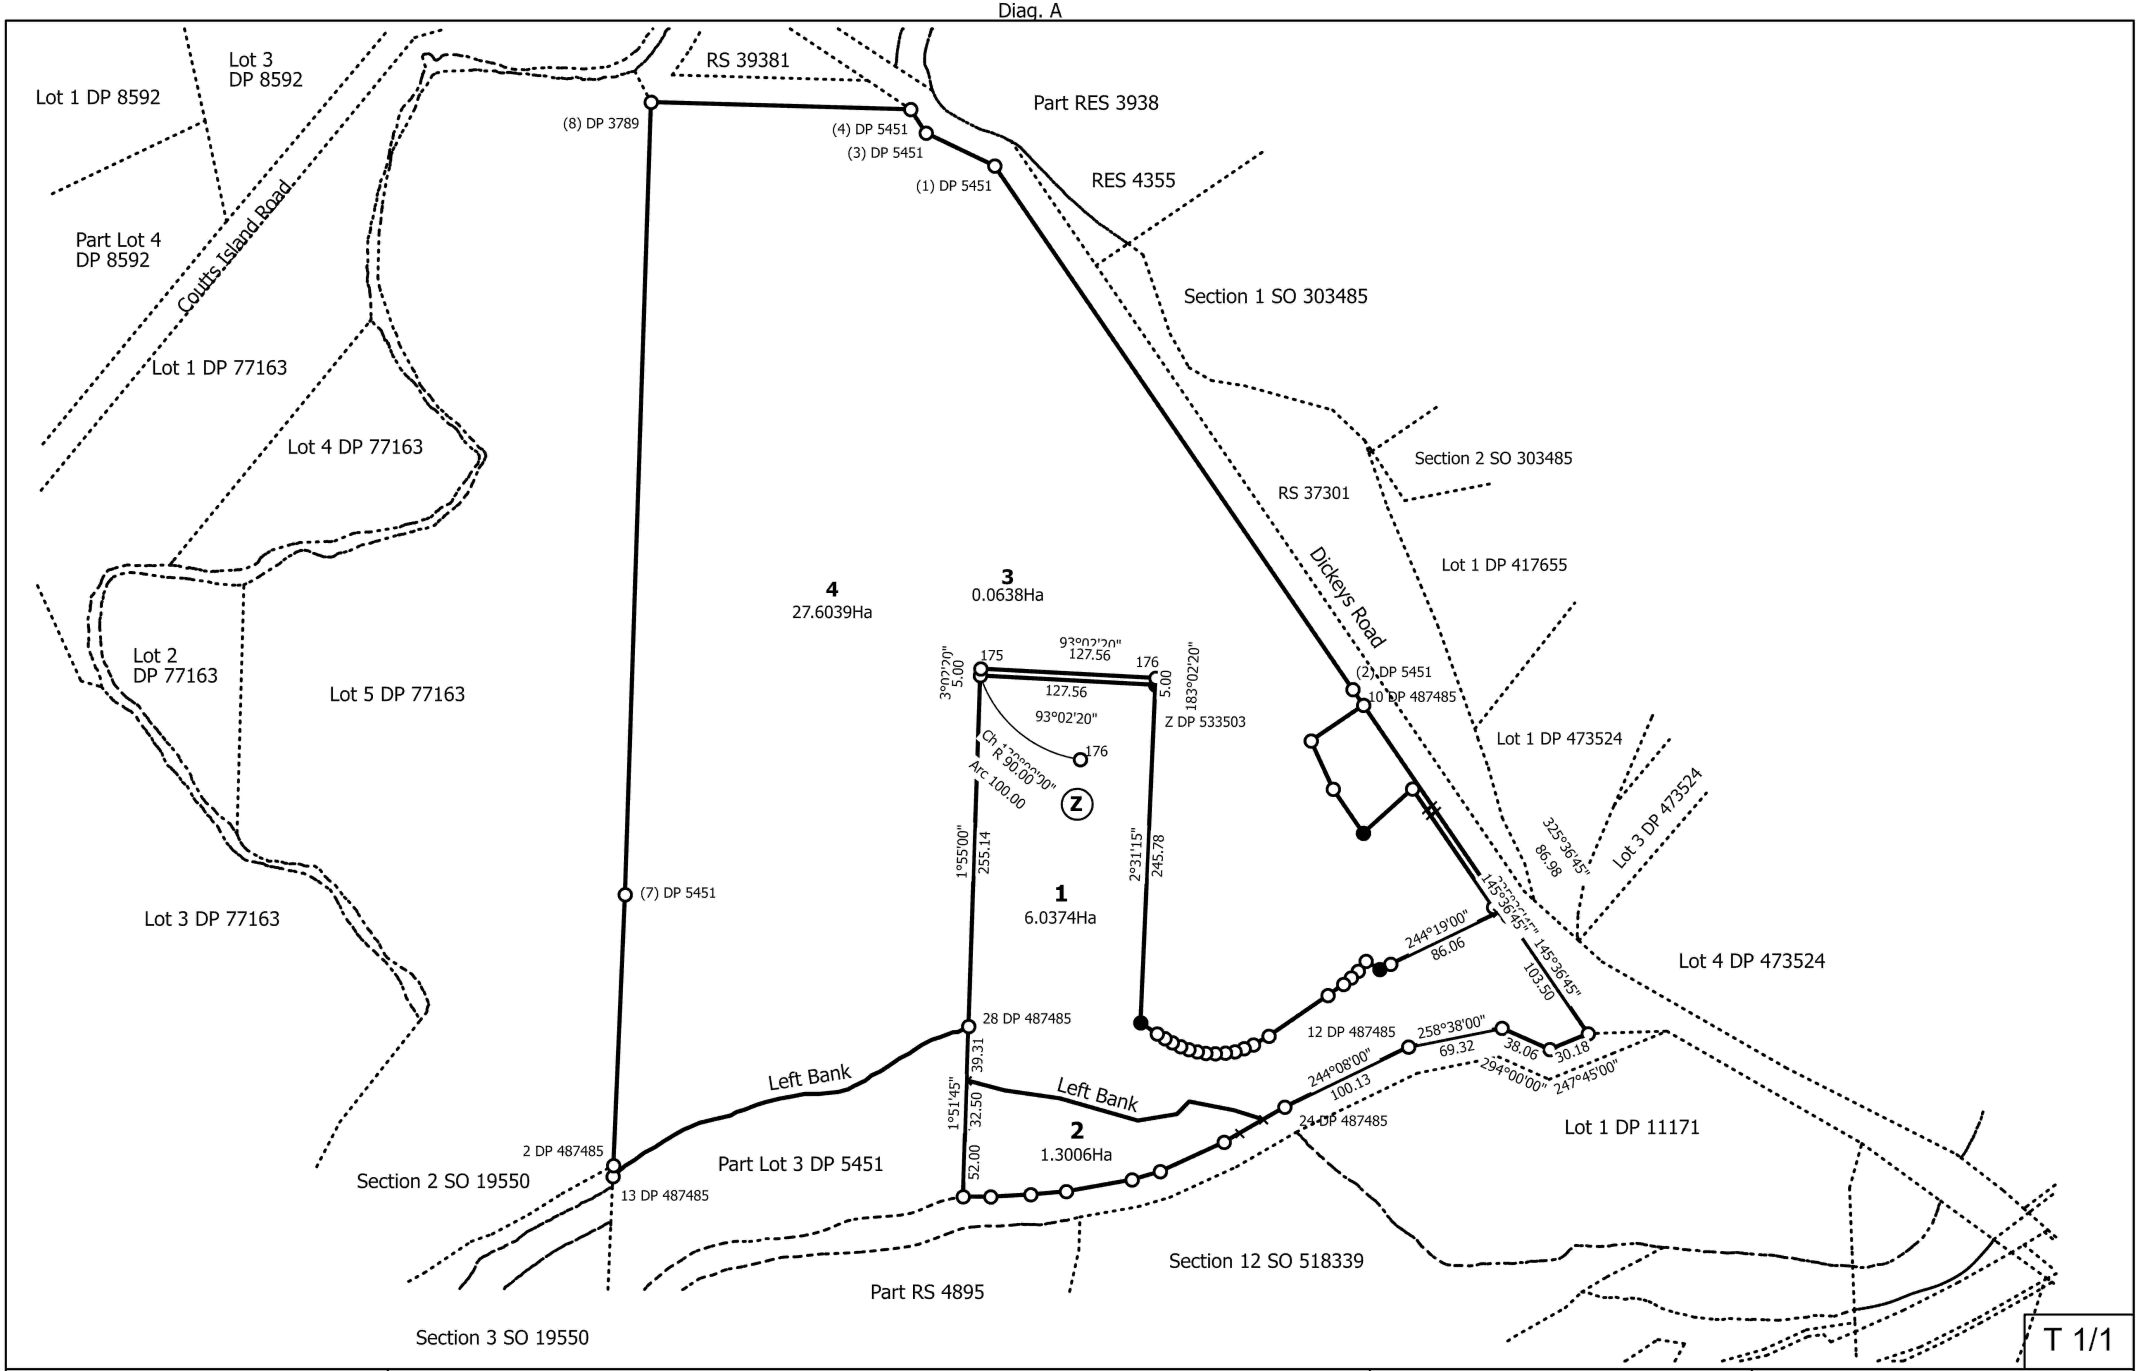

T 1/1

Land District: Wellington Digitally Generated Plan Generated on: 17 Sep 2024, 9:31am ...	Test Description	Surveyor: John Doe Firm: Test Corporate Na...	Record of Survey LT 99999